


NOTES:

1. ALL LEVELS IN METRES TO SHD. EXISTING RECLAIMED PLATFORM AT +5.50m SHD.
2. PRE-CUT EXISTING GROUND LEVEL TO +4.00m SHD WITHIN THE SHEETPILE CUT-OFF WALL BEFORE OPEN-CUT EXCAVATION.
3. OPEN-CUT BATTERS: 1V:2.5H IN FILL / MG ABOVE -6.00m SHD; 1V:1H IN OLD ALLUVIUM BELOW -6.00m SHD; 3m BERMES AT -6.00m SHD AND -12.00m SHD.
4. ACCESS RAMP 10m WIDE, GRADIENT 1:8.3, FROM -6.00m SHD TO -12.00m SHD. LOCAL SUMP 40m x 30m TO -21.60m SHD.
5. REFER TO SECTIONS C4, C4A, D2, D3 AND E4 (CIV-SD-90022 TO 90026) FOR SLOPE PROTECTION AND GIW.

N

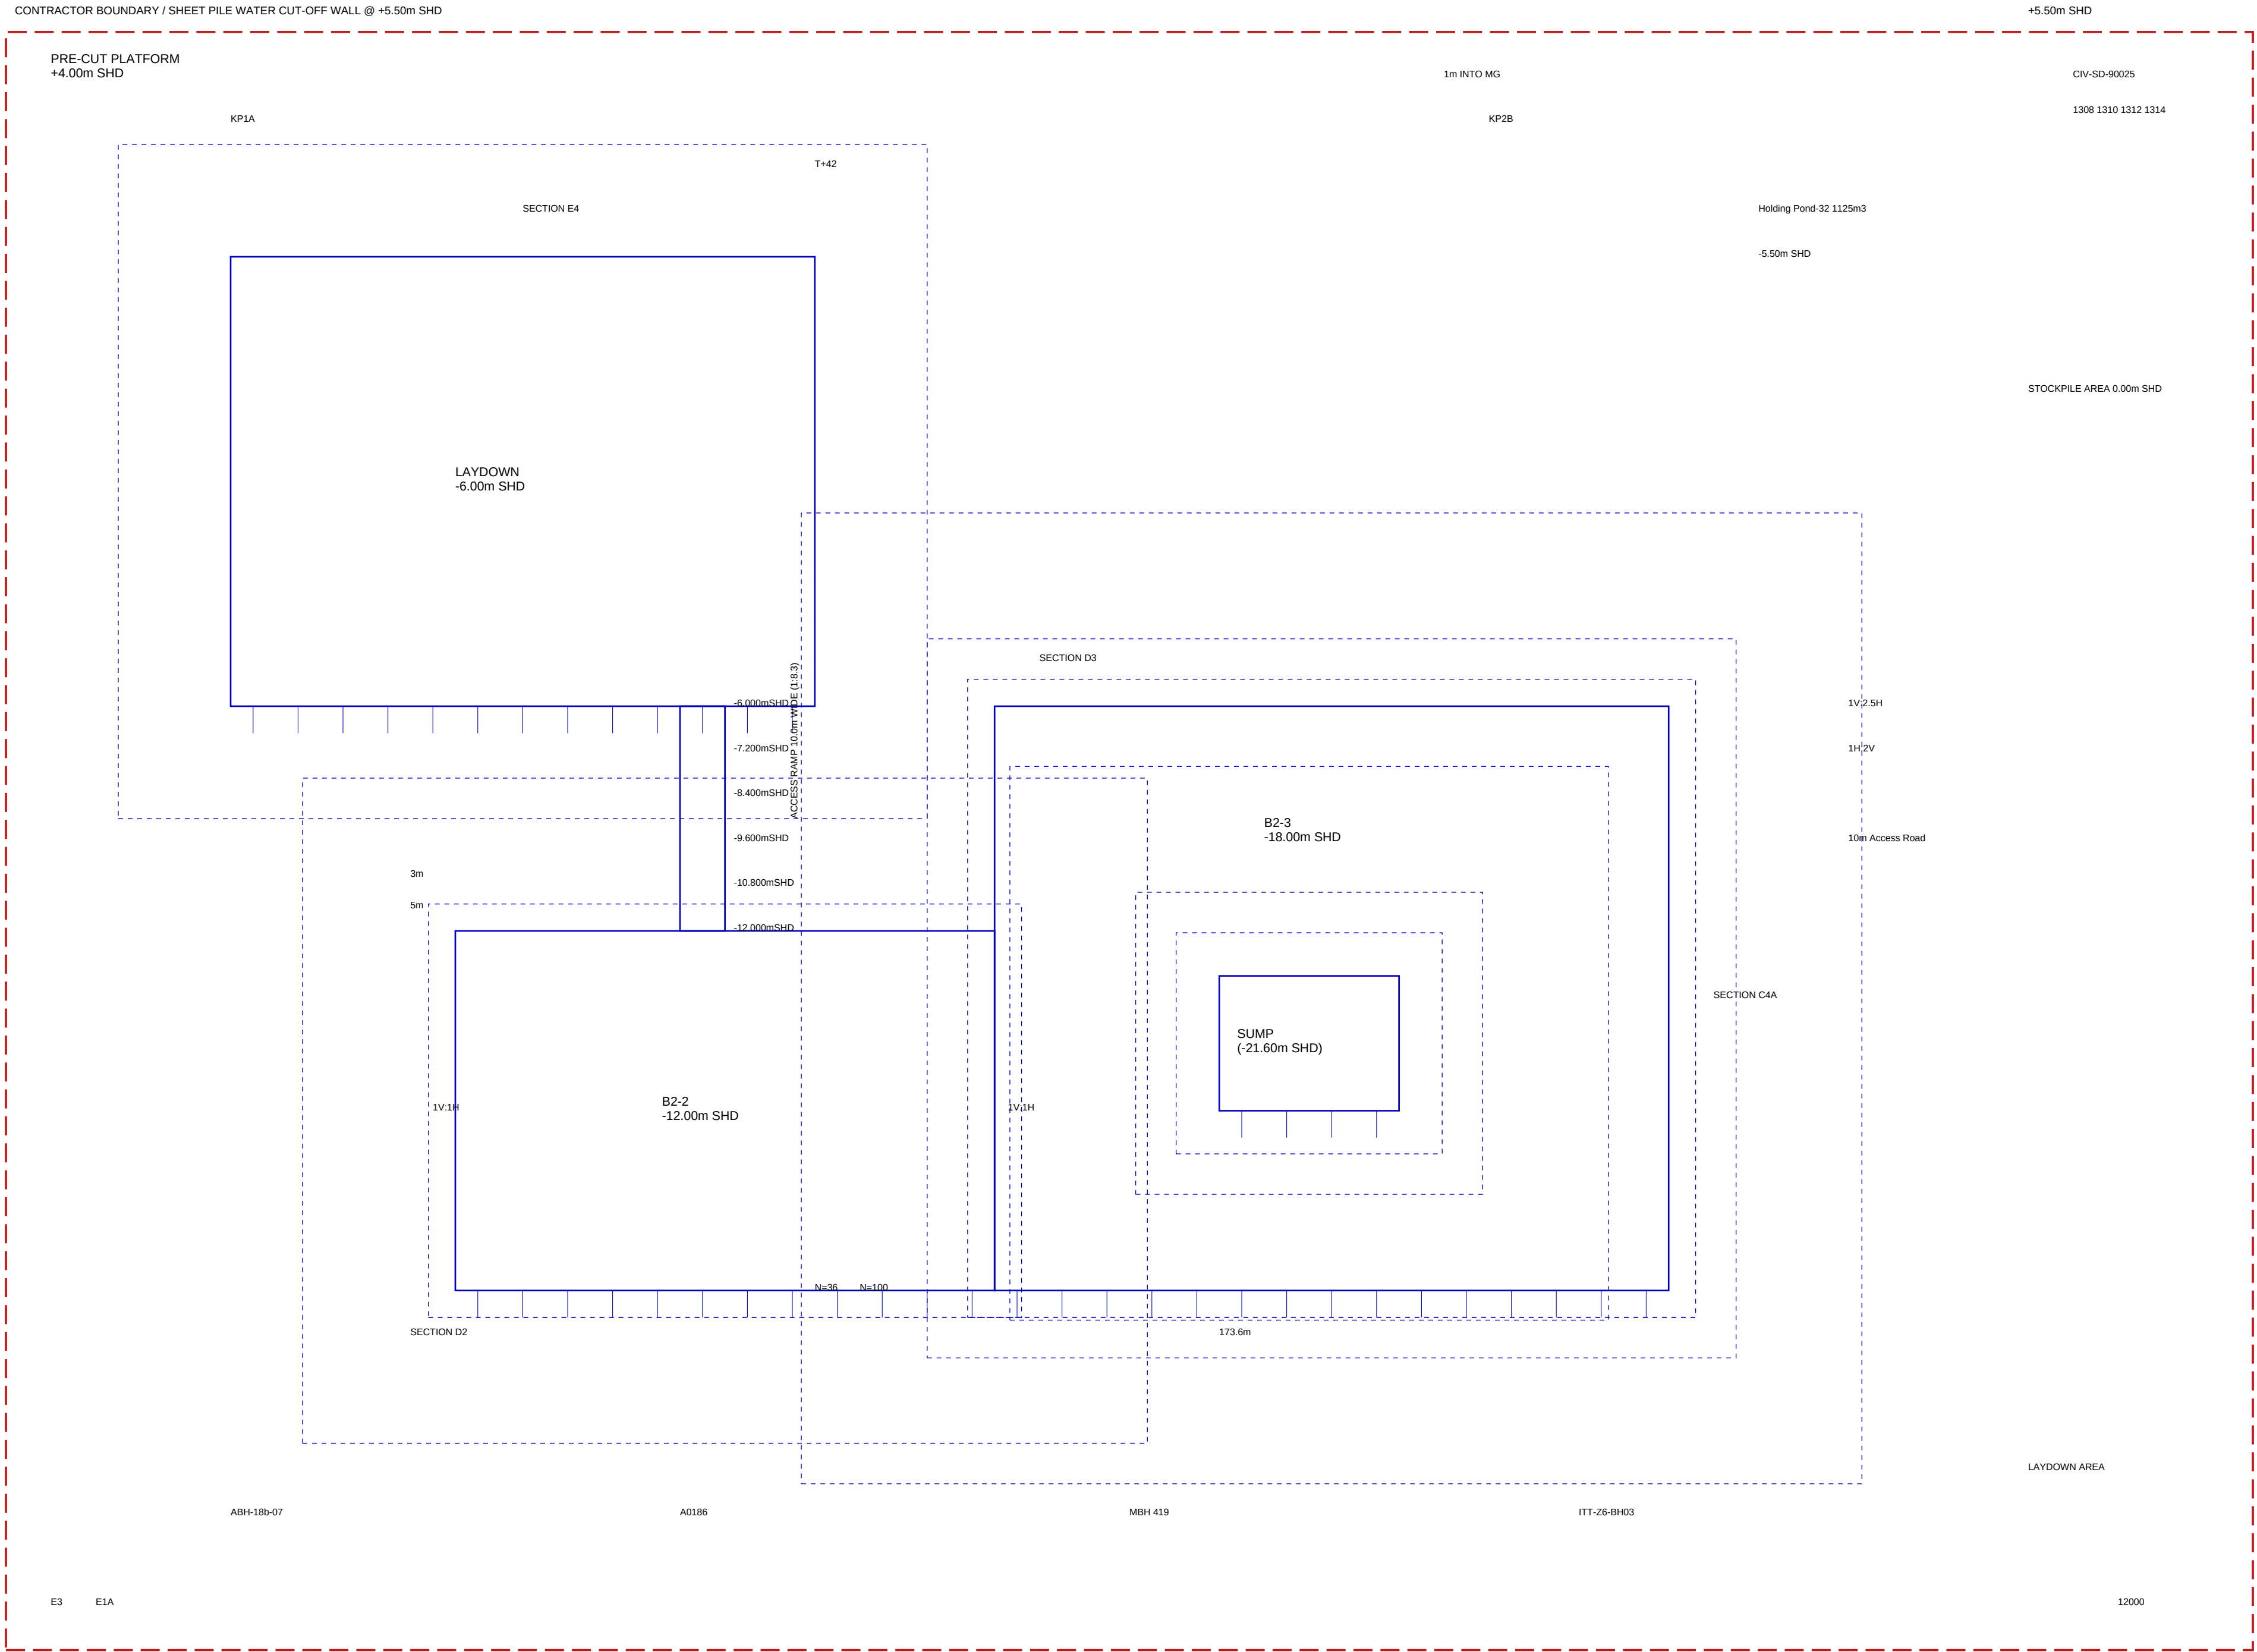

0 20 40 60 80 100 Metres Scale 1:1000

PROJECT TITLE: PROPOSED DEVELOPMENT OF A TERMINAL SUBSTRUCTURE (SAMPLE)

DRAWING TITLE: ERSS LAYOUT PLAN (FOR EXCAVATION)

MAIN CONTRACTOR: SAMPLE JV CONTRACTOR'S CAS CONSULTANT: SAMPLE GEO PTE LTD

DRAWING NO. XX-CIV-SD-20200 REV C1 STAGE S4 SUIT. CODE A SHEET SIZE A1

Scale: 1:1000 DATE 2024-07-15 DRAWN HK CHECKED ML APPROVED HTUN

CONFIDENTIAL - SAMPLE SHEET FOR SOFTWARE TESTING ONLY